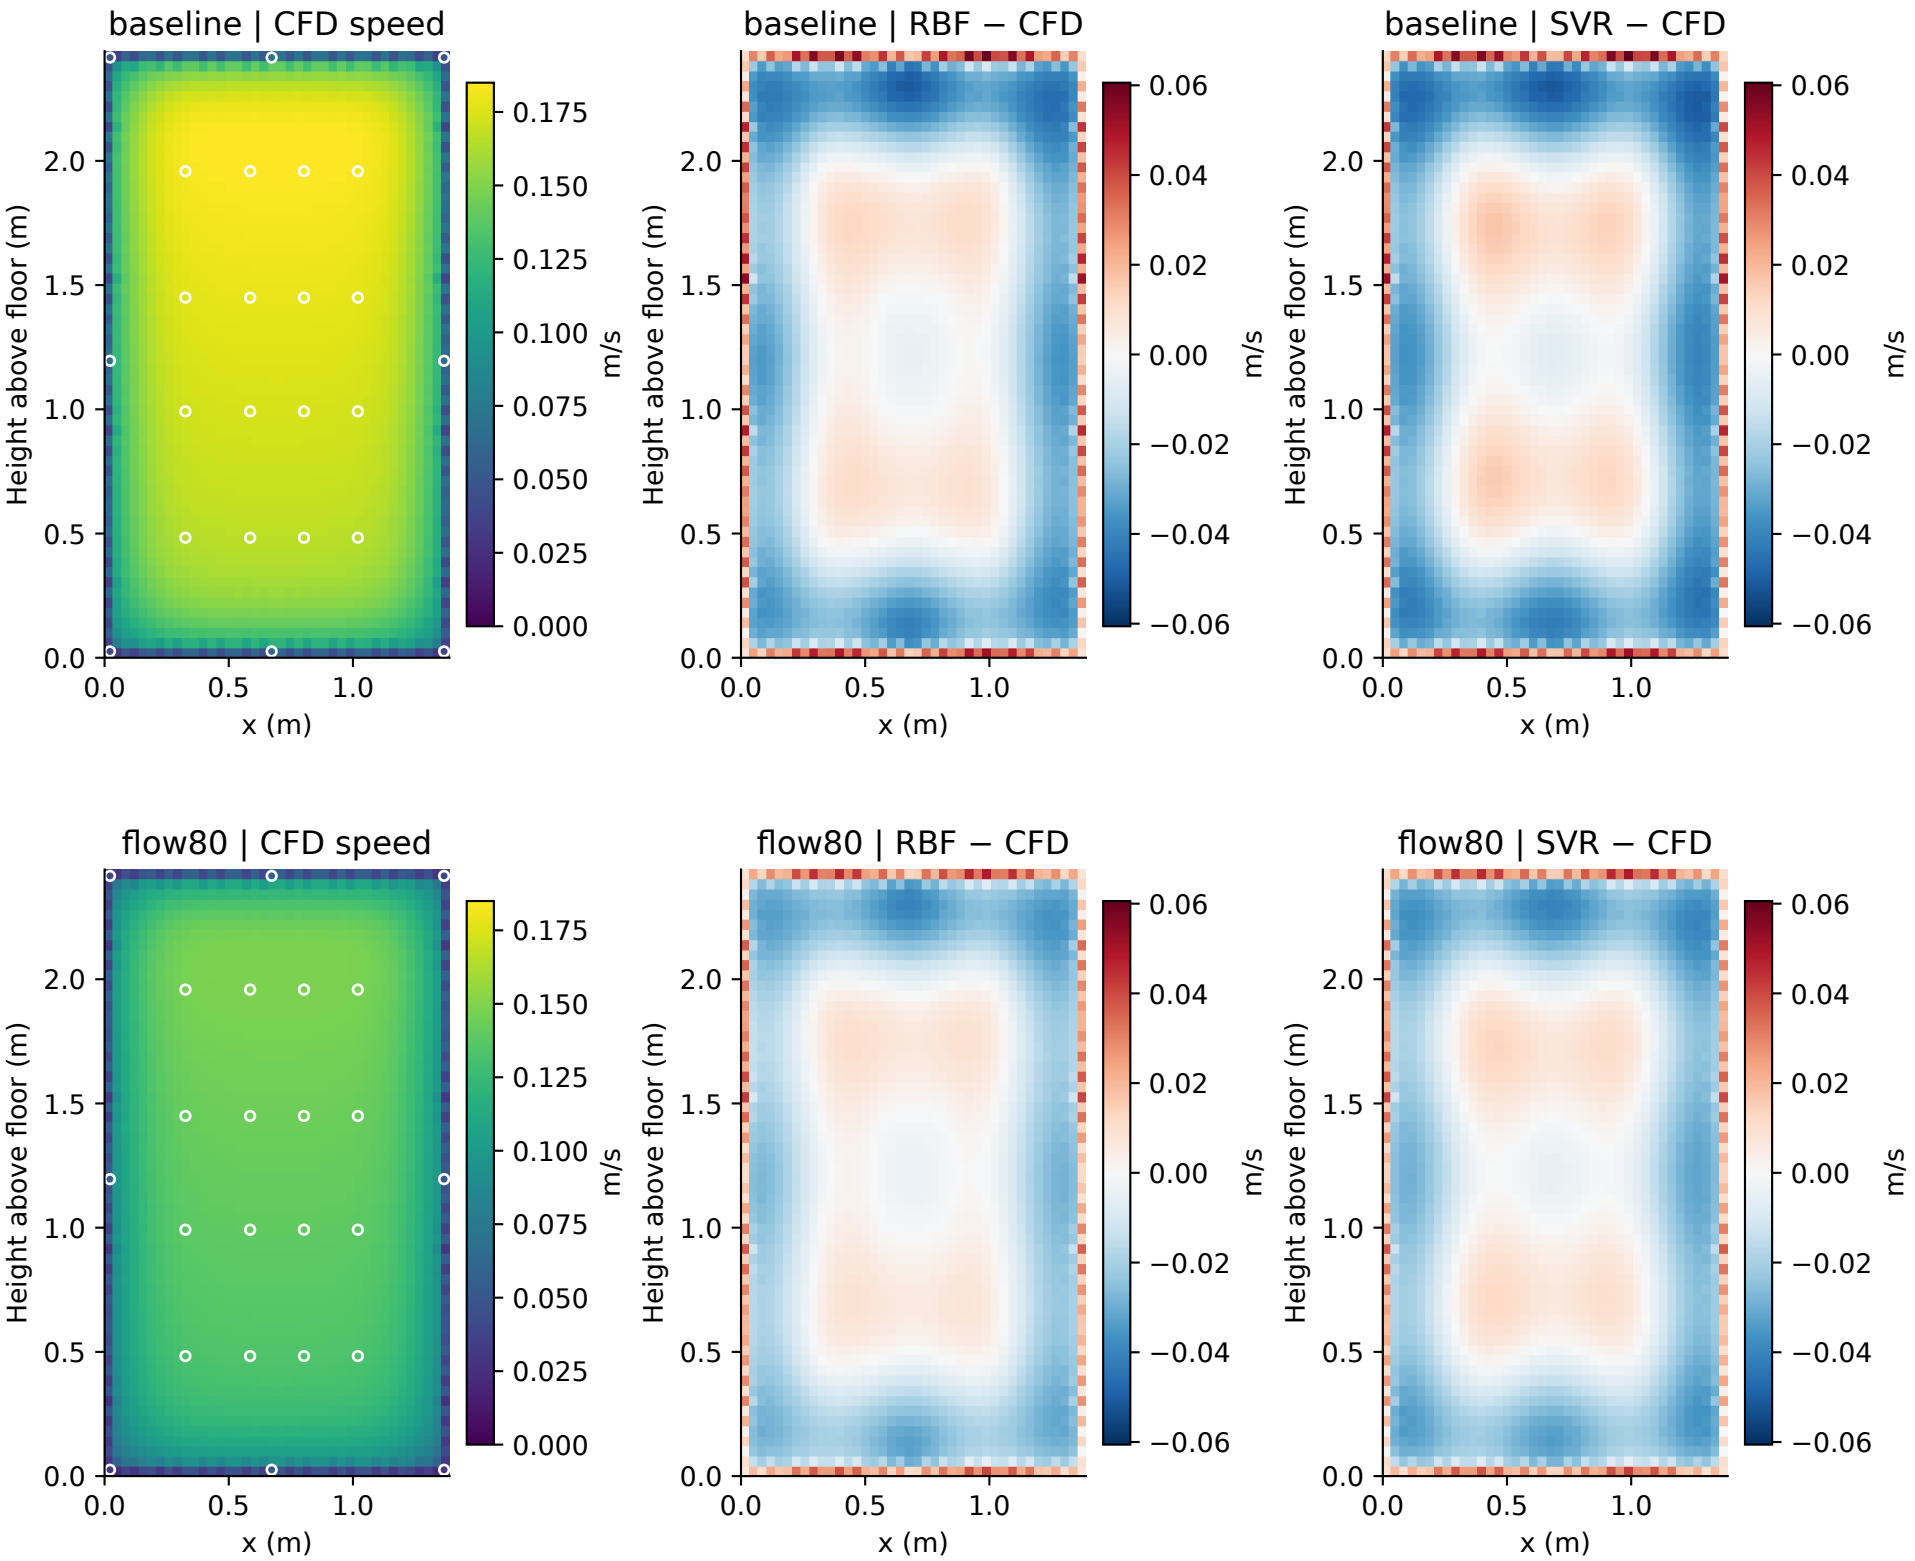

Fixed 24-sensor hybrid layout at 16 ft | models refitted on retained values
Numerical reconstruction only; common error scale across both flow cases
baseline | CFD speed
baseline | RBF − CFD
baseline | SVR − CFD
flow80 | CFD speed
flow80 | RBF − CFD
flow80 | SVR − CFD
Height above floor (m)
x (m)
m/s
0.000
0.025
0.050
0.075
0.100
0.125
0.150
0.175
−0.06
−0.04
−0.02
0.00
0.02
0.04
0.06
0.0
0.5
1.0
1.5
2.0